


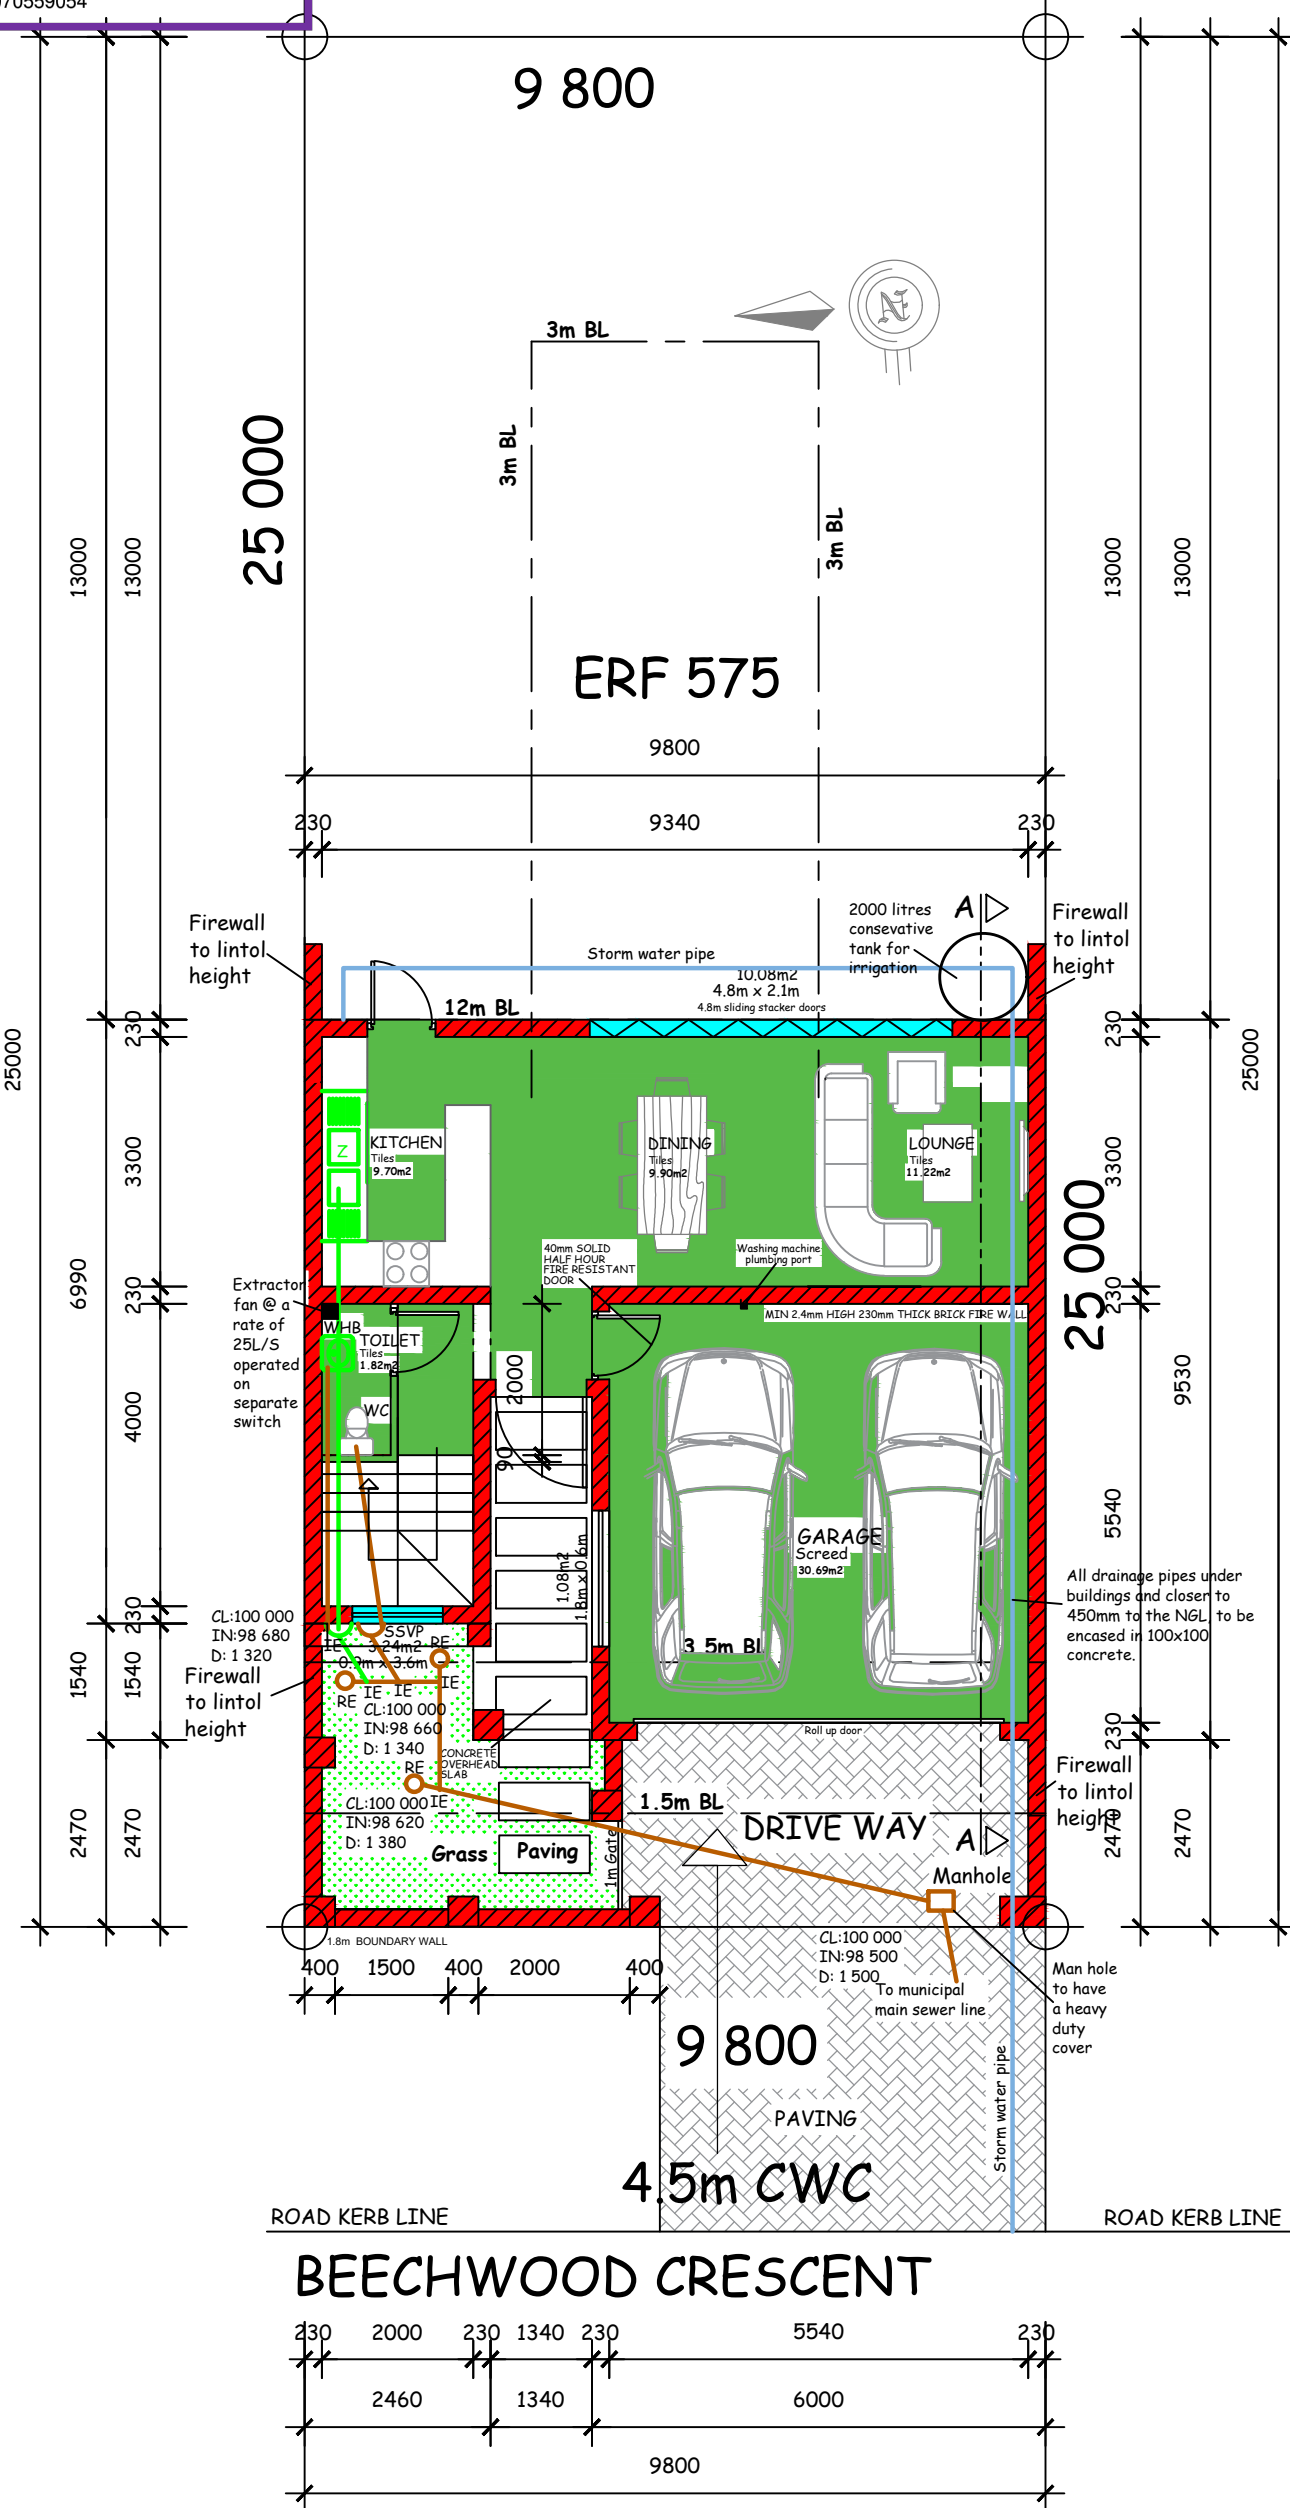

GROUND STOREY PLAN  
SCALE 1:100  
83.94m<sup>2</sup>

ENERGY EFFICIENCY REQUIREMENTS AND  
SANS 10400 XA

Fenestration areas (First Floor)  
Windows 9.27m<sup>2</sup>  
Floor 39.81m<sup>2</sup>  
Fenestration 23.29%

Hot water supply 300Litres  
Hot water to be used. (Solar)  
50% of water to be generated by Solar.

Lighting  
Low energy lighting to be used.

Roof Insulation  
115mm minimum cellulose fibre loose fill.  
Total R-Value of roof to total 3.7


ENERGY EFFICIENCY REQUIREMENTS AND  
SANS 10400 XA

Fenestration areas (Ground Floor)  
Windows 10.08m<sup>2</sup>  
Floor 39.21m<sup>2</sup>  
Fenestration 25.78%


Hot water supply 300Litres  
Hot water to be used. (Solar)  
50% of water to be generated by Solar.

Lighting  
Low energy lighting to be used.


Roof Insulation  
115mm minimum cellulose fibre loose fill.  
Total R-Value of roof to total 3.7

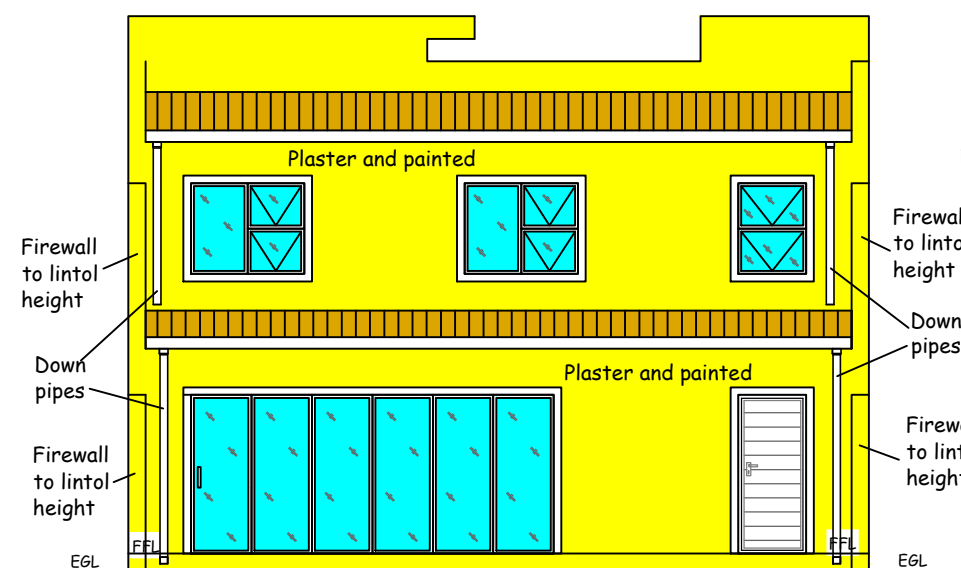


EAST ELEVATION  
SCALE 1:100

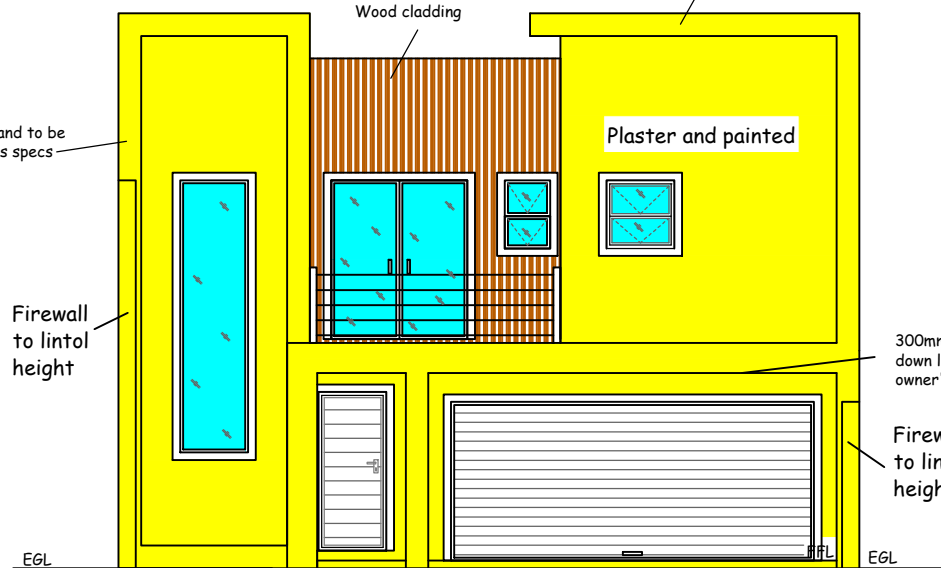


WEST ELEVATION  
SCALE 1:100

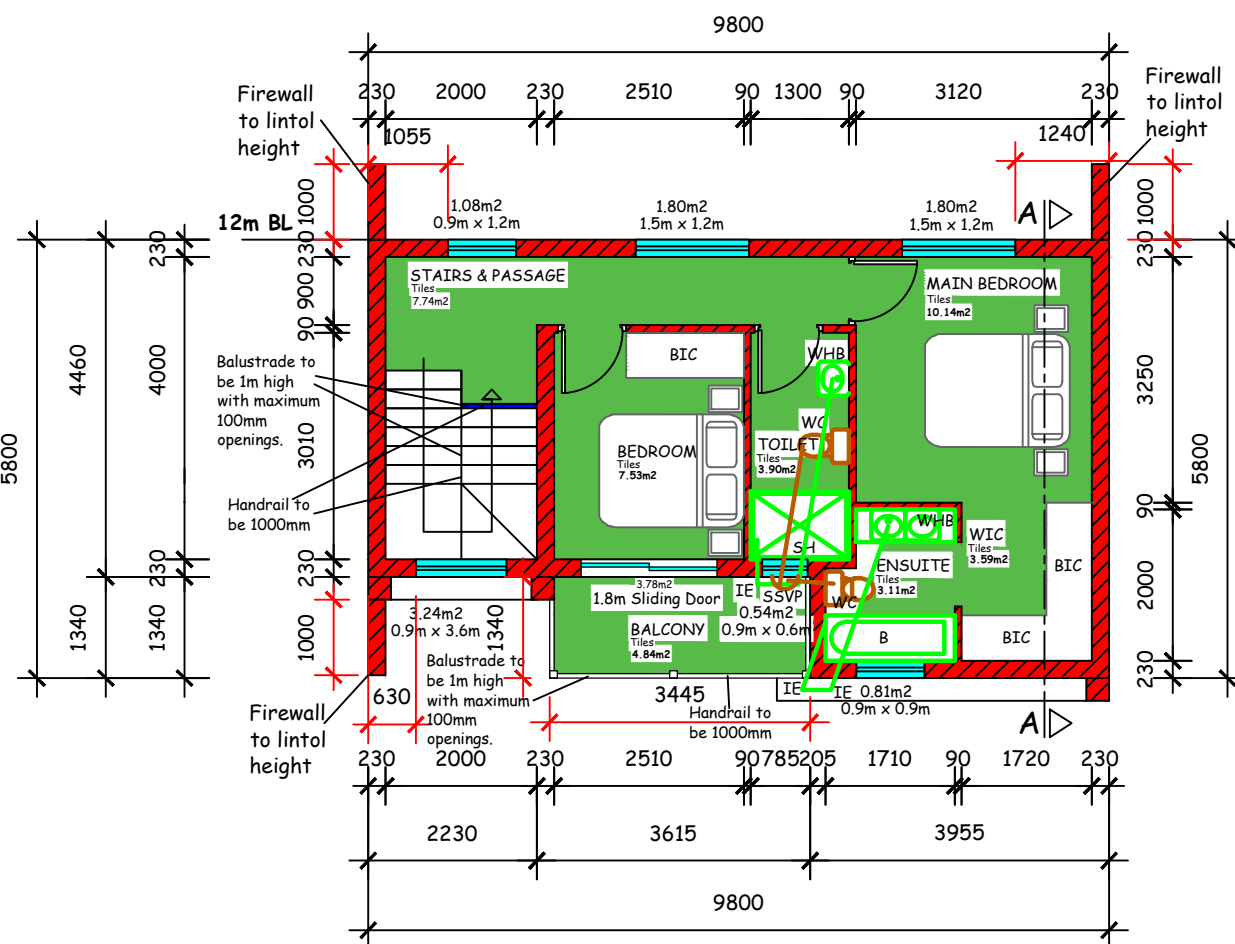

FIRST STOREY PLAN  
SCALE 1:100  
46.77m<sup>2</sup>

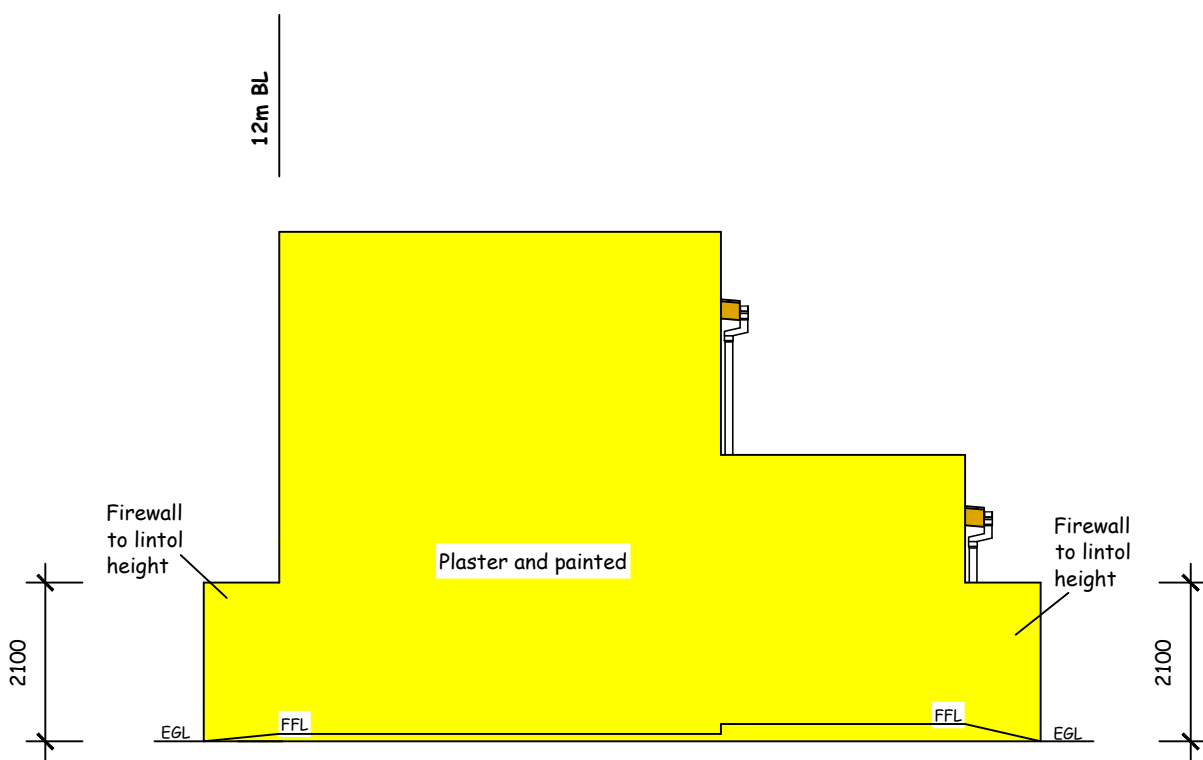

SOUTH ELEVATION  
SCALE 1:100

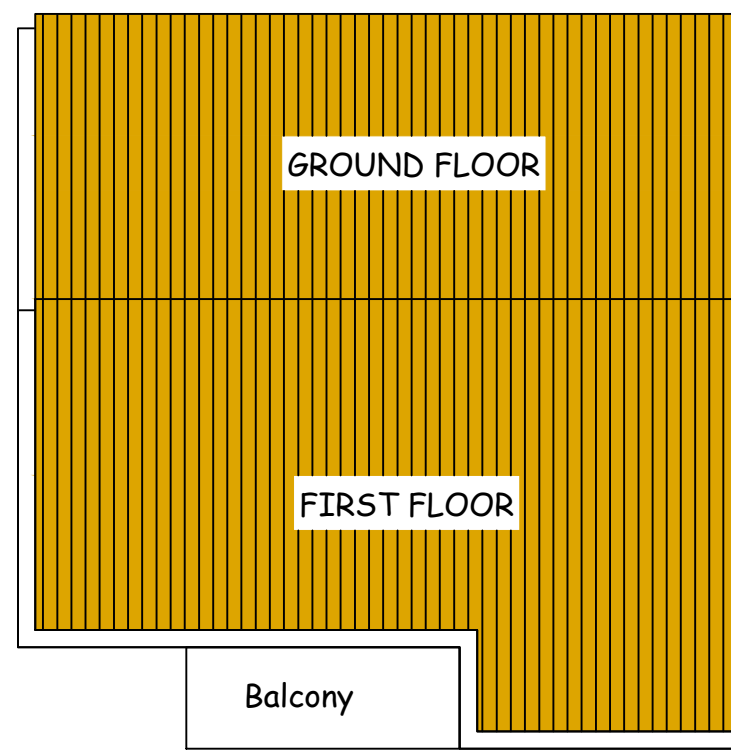


ROOF PLAN  
SCALE : NTS

- General Notes
- All works in compliance to NBS.
  - Brick force every 3rd course.
  - Brick force in every row above lintels.
  - Light area to be min 10% and ventilation area to be min 5% of all habitable rooms.
  - Disposal of stormwater to comply with part N of NBS.
  - Disposal of stormwater to comply with the requirements of part R of NBS and BS(Act 1030 of 1977).
  - All internal sewer pipe connections to be converted to closed systems.
  - RE to all ends.
  - IE to all bends.
  - Soil pipes to be min 110mm.
  - Waste pipes to be min 50mm.
  - Min fall of all pipes to be 1:40.
  - All material used to be SABS approved.
  - Fit gutters and down pipes where necessary.
  - Disposal of stormwater to comply with the requirements of part R of NBS and BS(Act 1030 of 1977).
  - All internal sewer pipe connections to be converted to closed systems.


Roof Notes  
Corrugated sheets on 76x50 purlins @ 1000c/c  
on 228x76 rafters @ 1050c/c, fixed to a  
114x38 wallplate to be tied to hoop iron ties  
600 deep in brickwork.  
Slope to be 5 degrees.

Ceiling notes  
Rhino board ceiling on 38x38 bracing at  
300c/c.135mm insulation above ceiling.

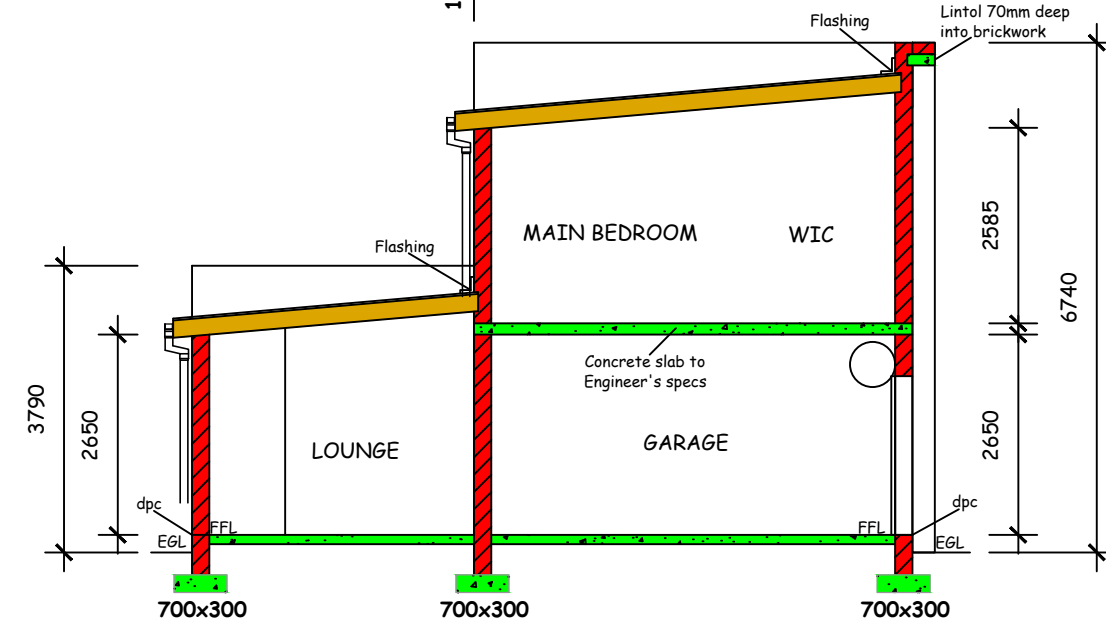


SECTION A-A  
SCALE 1:100

Floor notes  
25mm screed on 75mm concrete bed on  
100mm insulation on dpc on well  
compacted filling compacted  
in layers of 150mm.

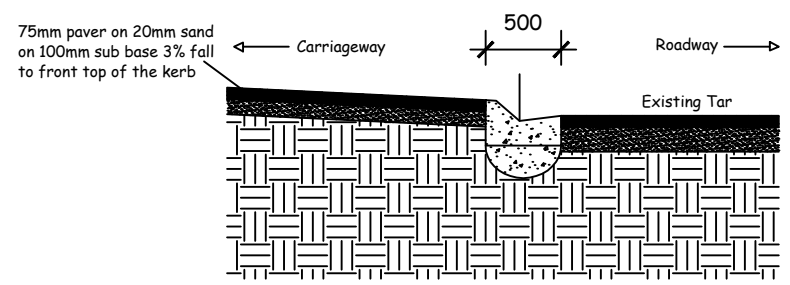


KERB SECTION DETAIL  
SCALE 1:50

Notes on SANS 10400PART XA:  
Perimeter insulation is required and is to be a minimum  
insulation with R-value of 1.0.  
Brickwall to have an insulation with R-value of 1.0 and a  
CR-value of 130.  
115mm flexible fibre glass blanket to be placed in the roof  
of the ceiling.  
All windows to aluminium frames.  
External doors to have seals for draught protection.  
Hot water pipes to be insulated with insulation that has a  
R-value of 1.0.  
Hot water tank and geyser to be insulated with insulation  
blanket with a R-value of 2.0.

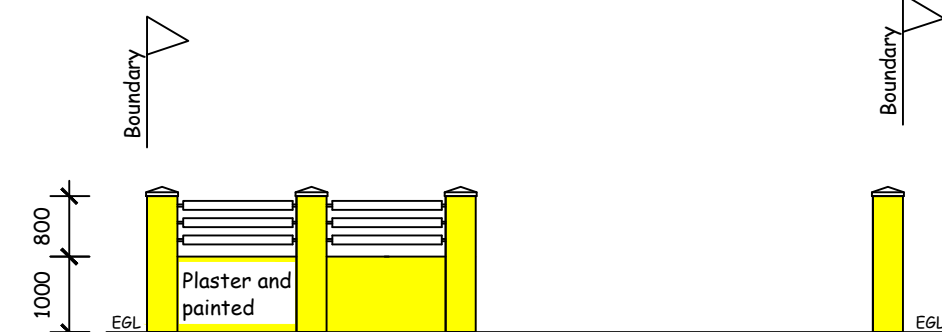


WEST BOUNDARY ELEVATION  
SCALE 1:100

Wall Calculations (Excluding gate)  
Wood slates area 3(140mm x 3000mm) 1.26m<sup>2</sup>  
Pillars 4(400mm x 1800mm) 2.88m<sup>2</sup>  
Solid wall area (1000mm x 3000mm) 3.00m<sup>2</sup>  
Total wall area, Pillars and Slates 7.14m<sup>2</sup>  
Visible Area(680mm x 3000mm) 2.04m<sup>2</sup>  
Percentage (2.04 / 7.14)100% 28.57%

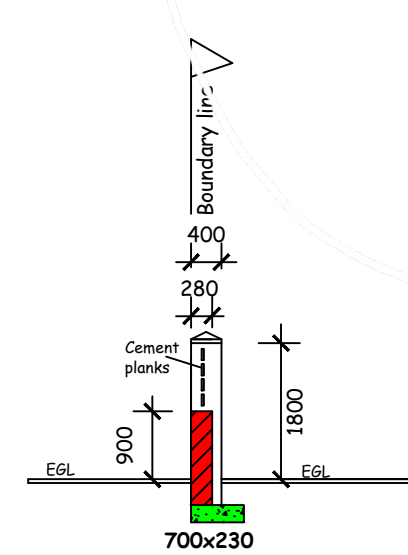

SECTION THROUGH  
BOUNDARY WALL  
SCALE 1:100

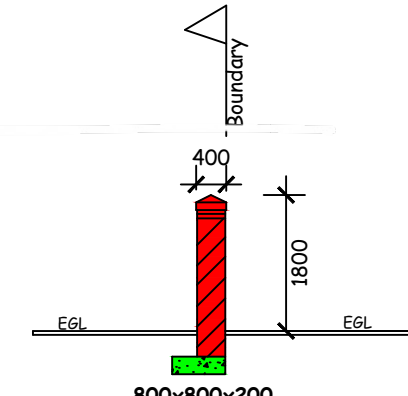

SECTION THROUGH PILLAR  
SCALE 1:100

Redacted for portfolio purposes.  
Confidential information  
removed.

Sketch Type: GROUND STOREY PLAN, FIRST STOREY, SITE PLAN, SECTIONS, ELEVATIONS AND NOTES

| Page   | Scale    | Date     | FLOOR FACTOR (1) | 245m <sup>2</sup>    | DRG  |
|--------|----------|----------|------------------|----------------------|------|
| 1 of 1 | AS SHOWN | Apr 2021 | Floor footprint  | 130.71m <sup>2</sup> | No.  |
|        |          |          | Factor           | 0.53                 | M185 |

Linear Calculations  
Permitted  
Linear covered

(10m+3.8m+10m)60% = 14.28m  
3.00m+1.03m+3.00m+1.03m+8.06m

Areas  
Ground Storey  
First Storey  
Total  
Footprint  
ERF size  
Coverage

83.94m<sup>2</sup>  
46.77m<sup>2</sup>  
130.71m<sup>2</sup>  
83.94m<sup>2</sup>  
245m<sup>2</sup>  
34.26 %